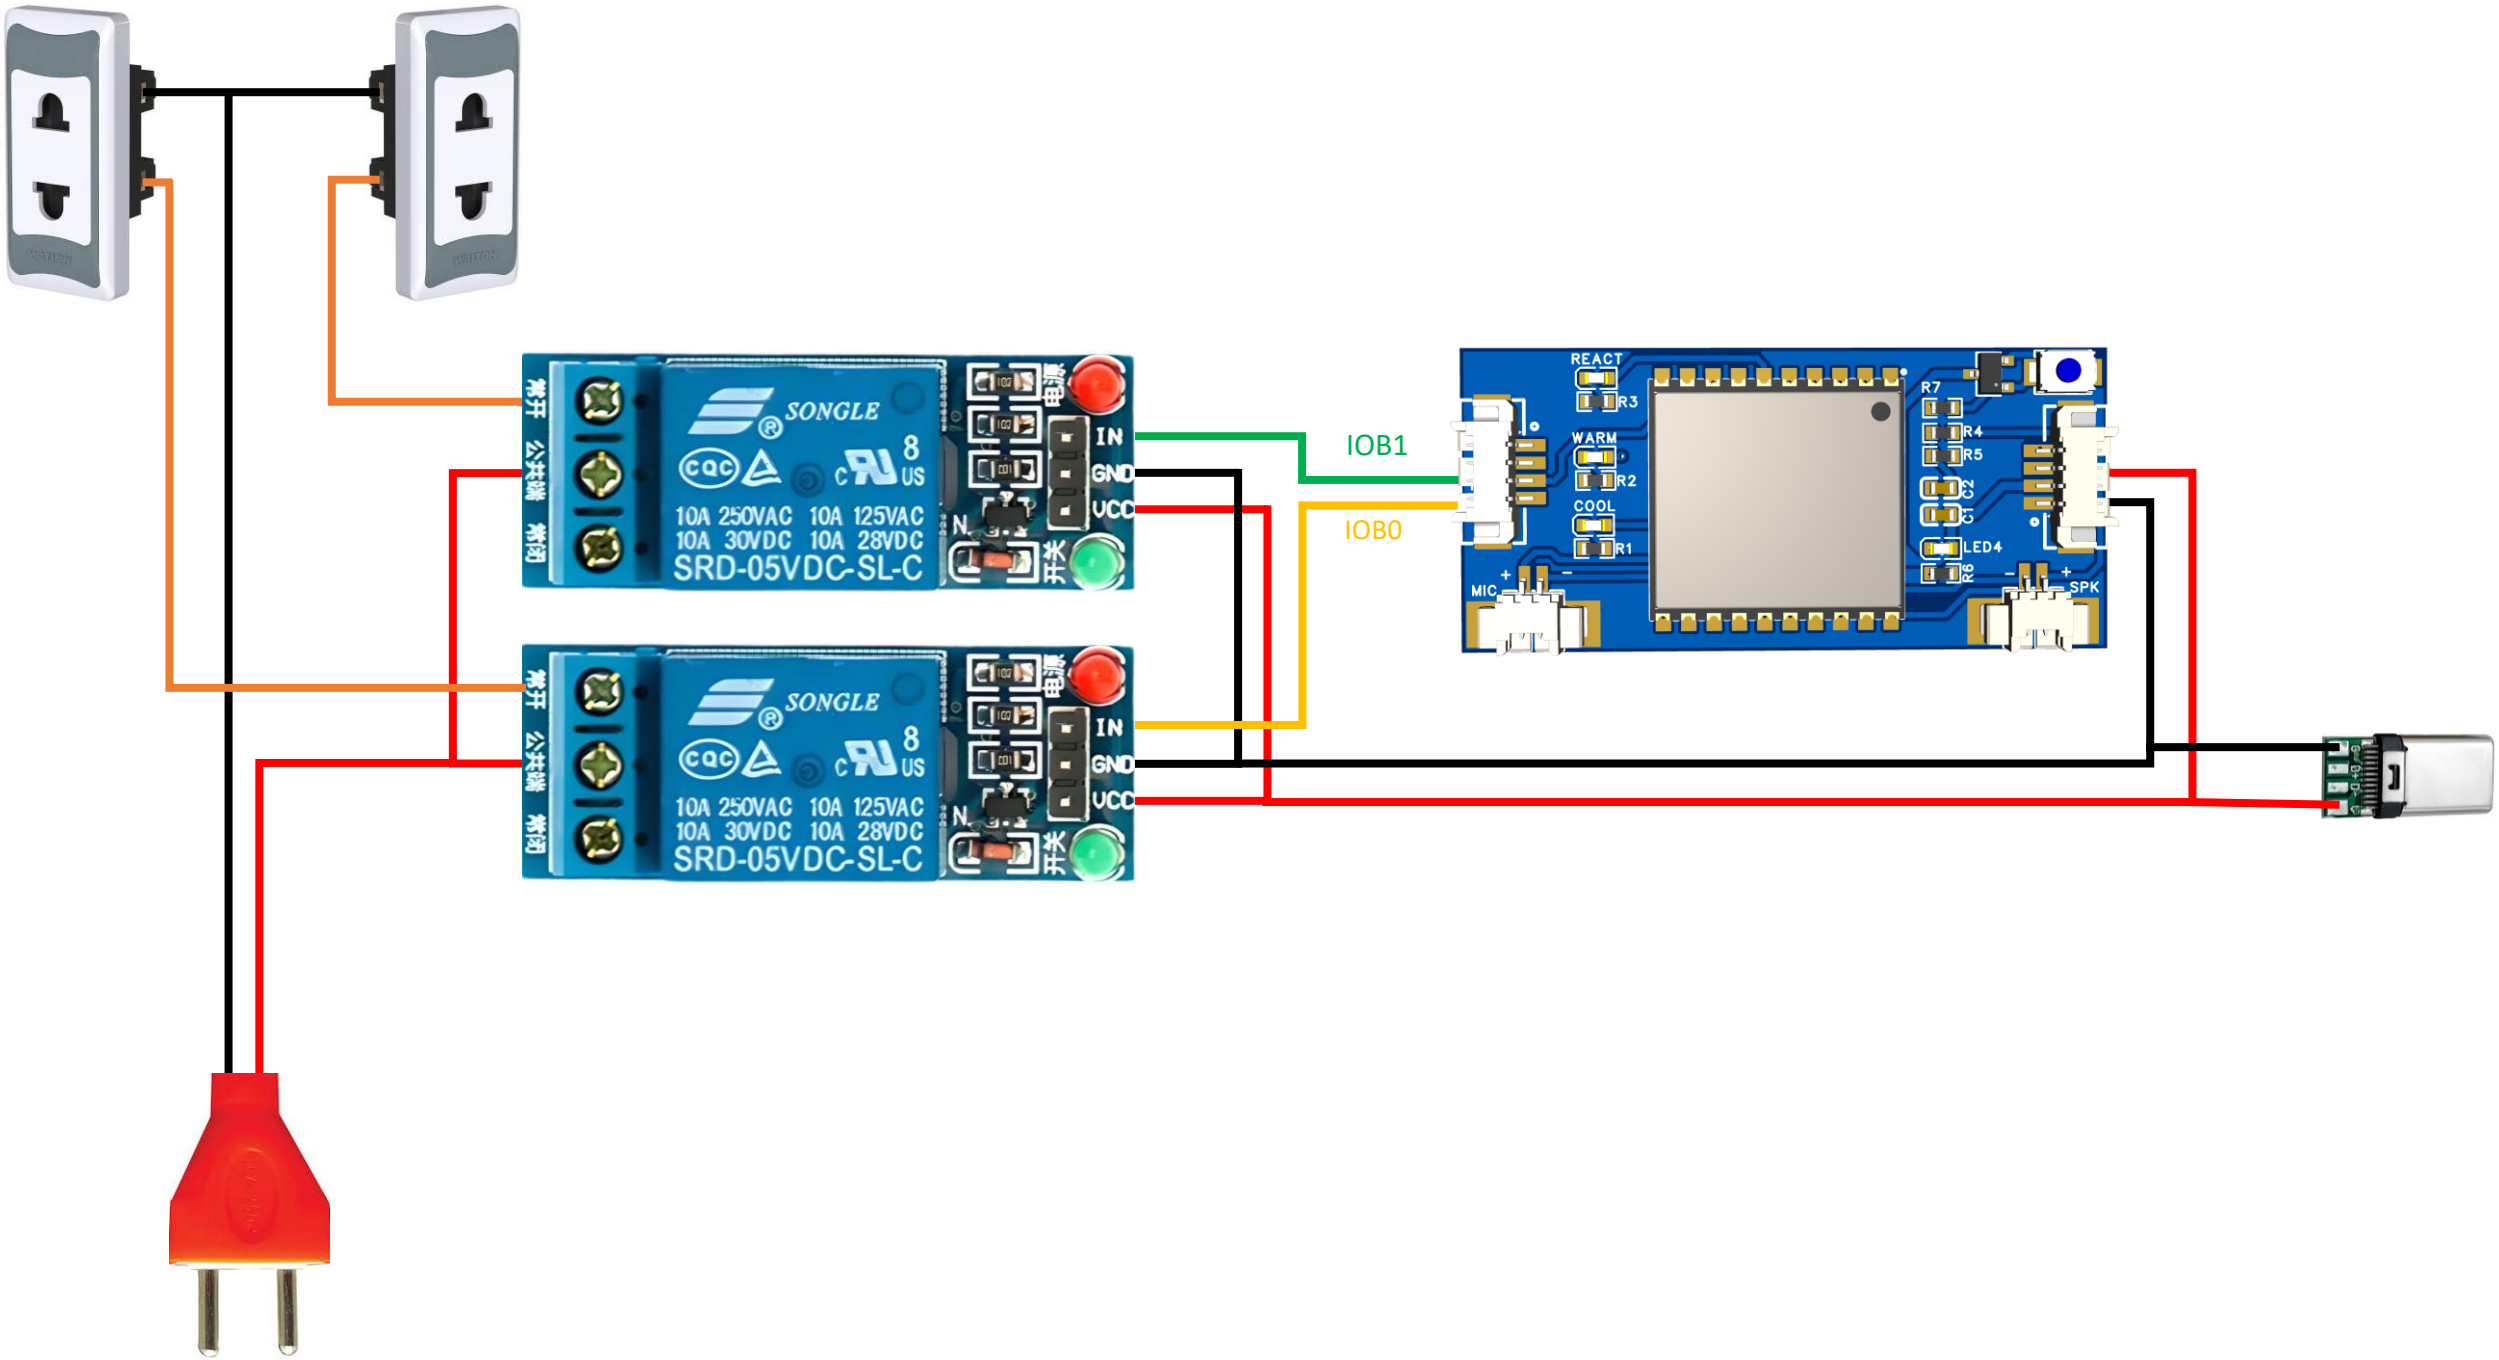

SONGLE
10A 250VAC 10A 125VAC
10A 30VDC 10A 28VDC
SRD-05VDC-SL-C
常开 公共端 常闭
电源
IN
GND
VCC
N
开关
IOB1
IOB0
REACT
R3
WARM
R2
COOL
R1
R7
R4
R5
LED4
MIC
SPK